FASĀDE ASĪS 1-5
1 : 100

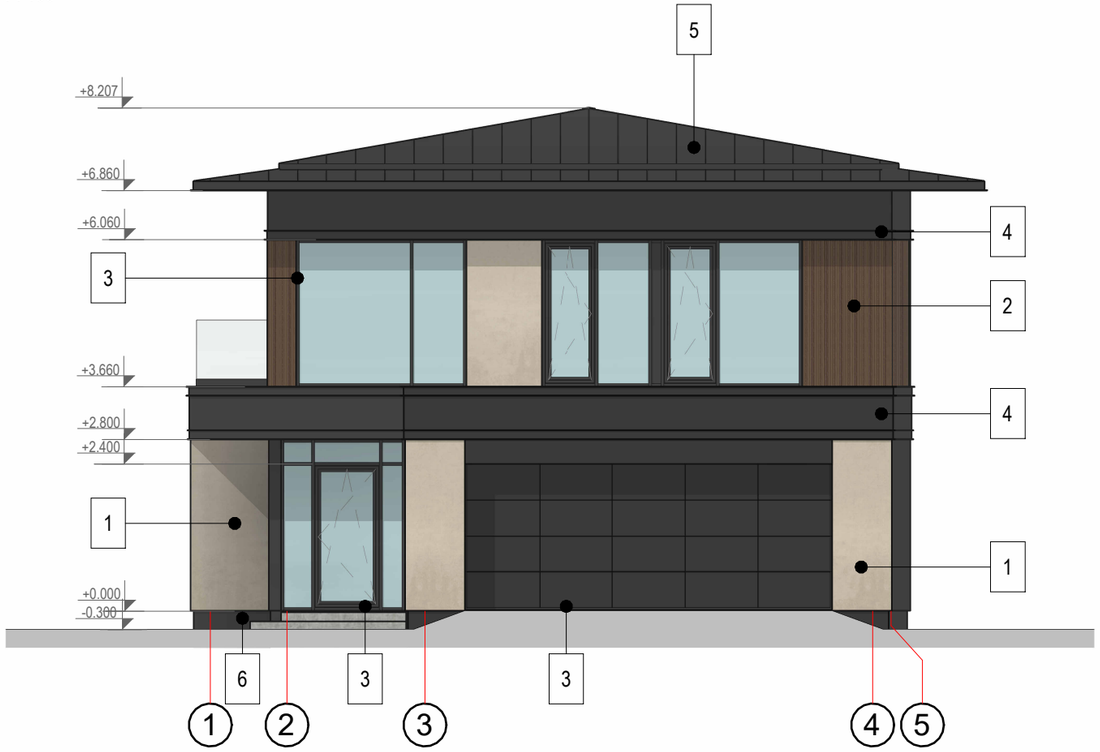

FASĀDE ASĪS A-E
1 : 100

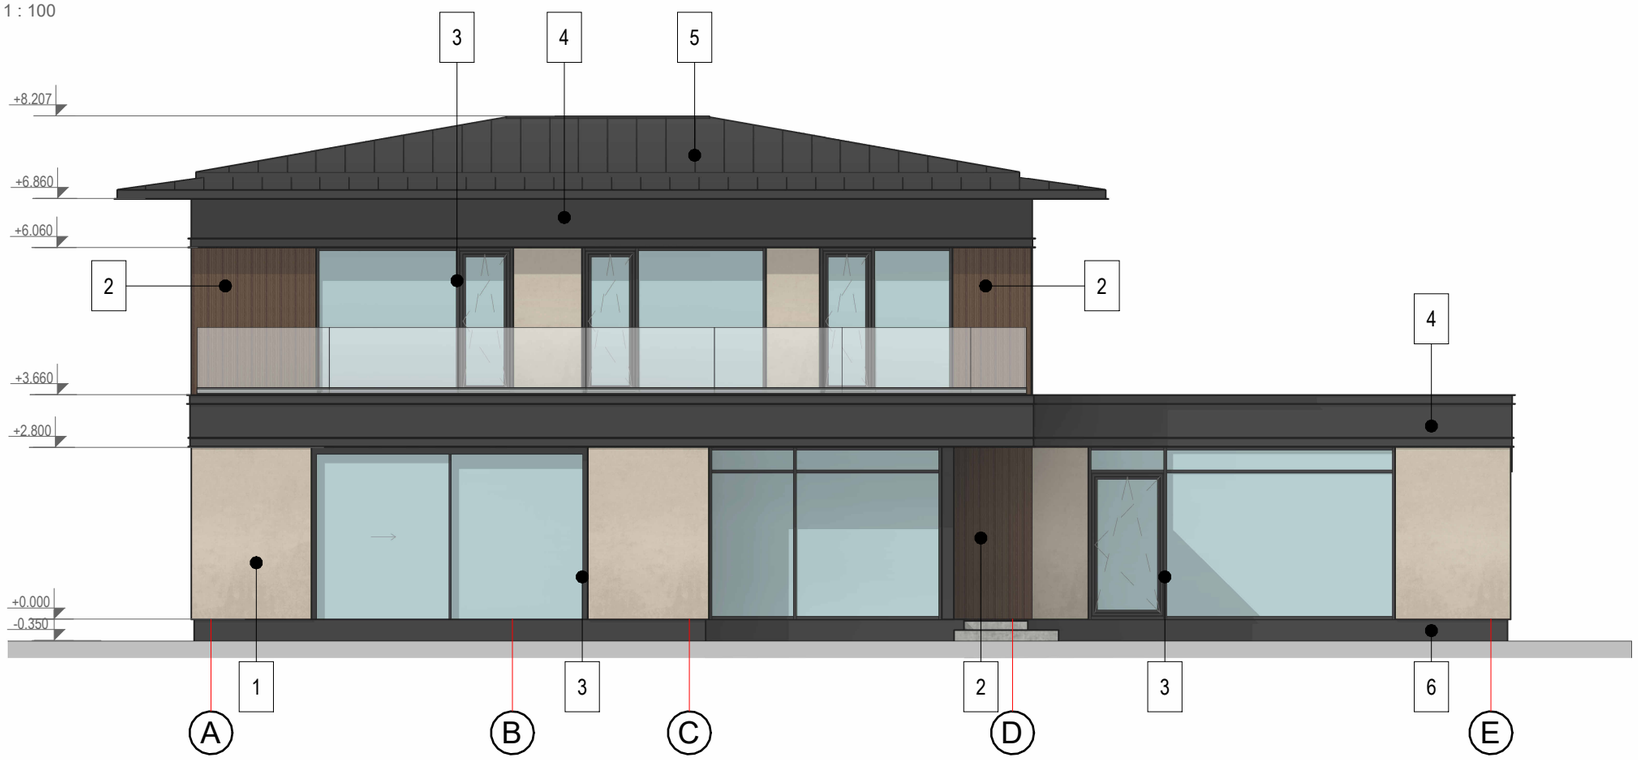

Piezīmes

1. Visi izmēri doti milimetros, augstuma atzīmes metros.
2. Par nosacīto 0.000 augstuma atzīmi pieņemts ēkas 1.stāva grīdas līmenis, kas atbilst augstuma atzīmei ±0.000=11.05m Latvijas augstumu sistēmā (LAS 2000,5).
3. Būvprojekta lapas skatīt visas kopā.
4. Rasējumus nemērīt, lasīt rakstītos izmērus
5. Krāsu toņi .pdf failā vai izdrukā neatbilst paredzēto apdares materiālu patiesajiem toņiem katra datora individuālo uzstādījumu dēļ.

FASāžU APDARES MATERIāLU SPECIFIKāCIJA

Nr.	Apzīmējums	Nosaukums	Piezīmes
1		Dekoratīvs apmetums	Capatect-ArmaReno Siena 50
2		Apdares dēļi	TERMO Taeda 20x140 RIMAS B
3		Logi, durvis un stikla sistēmu rāmji	Tonis Antracīts
4		Metāla detaļas	Tonis RR2H3 Antracīts
5		Classic Silence C jumta iesegums	Tonis RR2H3 Antracīts
6		Dekoratīvs apmetums - cokolam	Tonis Granit 10

BŪVP.VADĪTĀJS	Indulis Kalns
Izstrādāja	Indulis Kalns
Izstrādāja	Kalvis Lejasmeiers

Objekts — Pasūt.Nr. 02-03/2026

Dzīvojamās mājas būvniecība

Adrese
Gerberu iela 4, Mārupe, Mārupes nov., kad.Nr. 80760070058

Pasūtītājs
ANNIJA KĀRKLIŅA

FASĀDES ASĪS 1-5, A-E

Mērogs	Datums	Stadija	Lapa
1 : 100@A3	02.03.2026	MBP	AR-5

MI DESIGN
Jēkaba Dubelšteina iela 7-46, Liepāja, Latvija
+371 27 438 399